


C:\ES Projects\2017 Projects\Team TEM\17093 Apple Rehab Kent CT\Contract Documents\17093_P-120.dwg Plotted by cmassaro on Sep 10, 2020 - 4:03pm

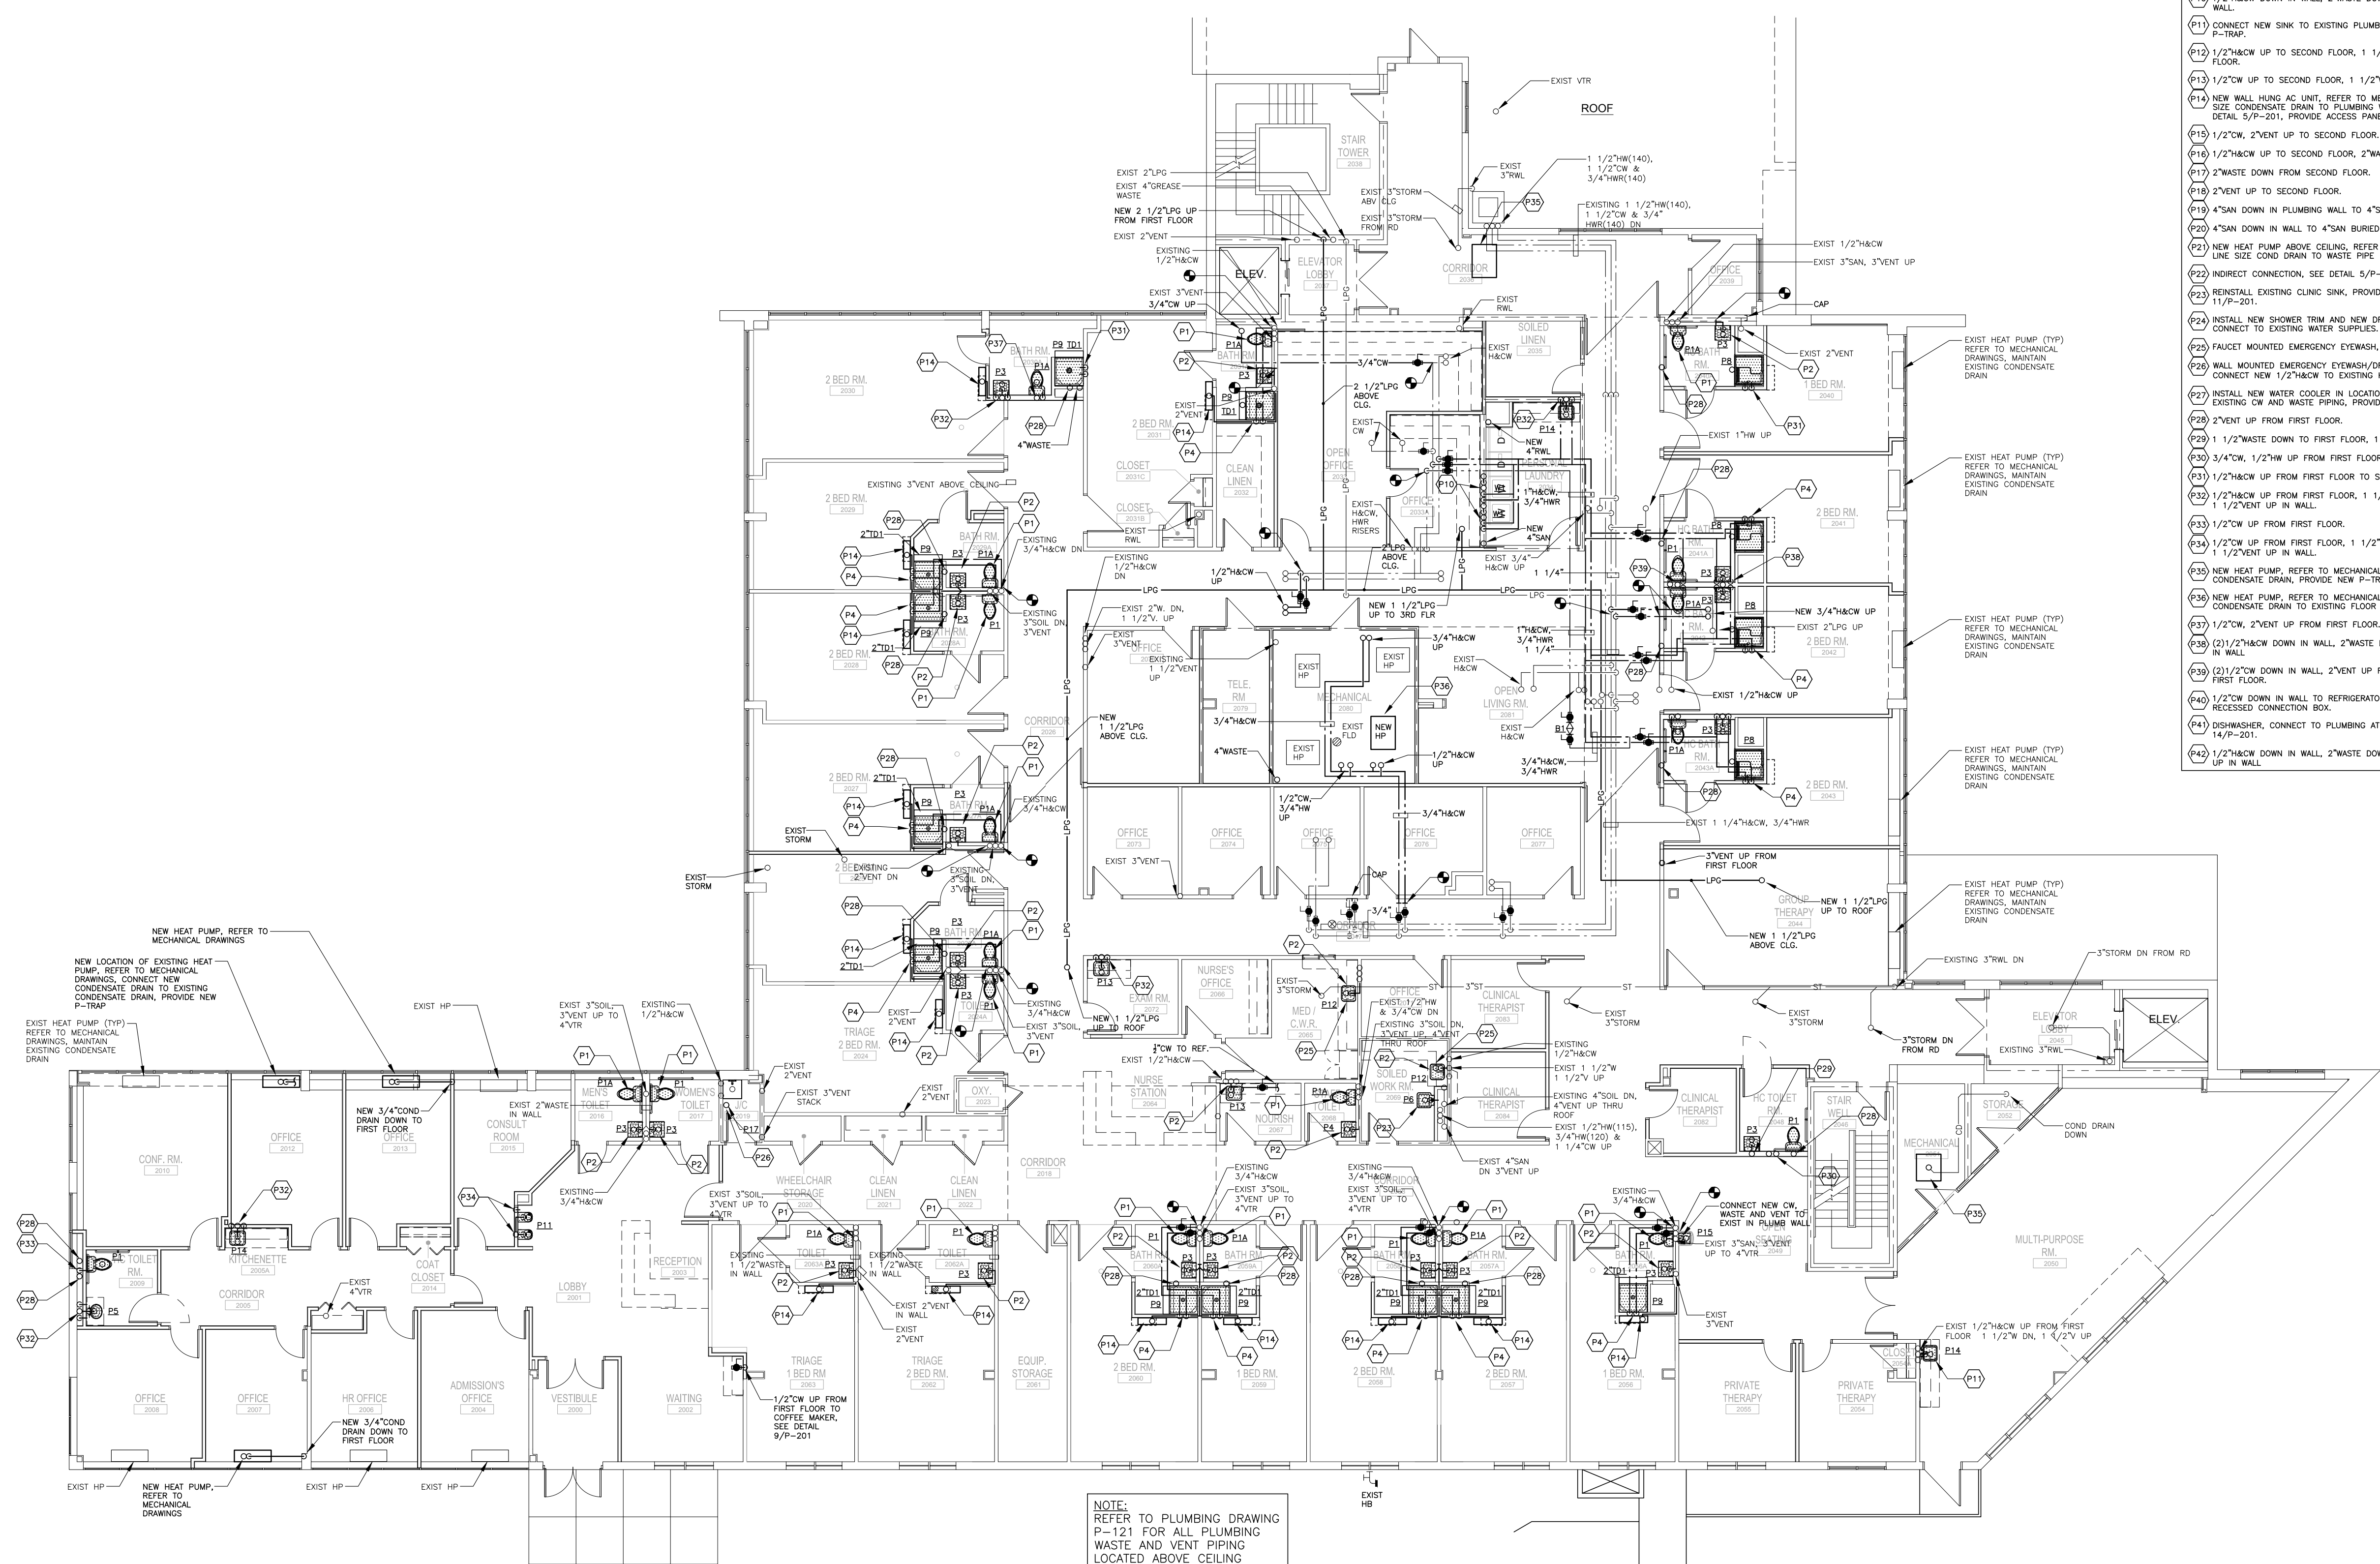

ISOLATION VALVE ACCESS NOTE

ALL ISOLATION VALVES SHALL BE LOCATED ABOVE AN ACCESSIBLE CEILING, NO ISOLATION VALVES SHALL BE INSTALLED IN PATIENT ROOMS OR PATIENT BATHROOMS REGARDLESS OF THE CEILING PROVIDED.


NEW CONCEALED PLUMBING PIPING

CONTRACTOR SHALL BE RESPONSIBLE FOR CUTTING OPEN EXISTING WALLS AS REQUIRED FOR THE INSTALLATION OF NEW PLUMBING PIPING. CONTRACTOR SHALL ALSO BE RESPONSIBLE FOR PATCHING EXISTING WALLS, PATCH SHALL MATCH EXISTING.

- PLUMBING KEY NOTES**
- (P1) INSTALL NEW TOILET IN LOCATION OF THE REMOVED TOILET, CONNECT TO EXISTING SANITARY & CW SUPPLY, PROVIDE NEW CW STOP.
 - (P2) INSTALL NEW SINK IN LOCATION OF REMOVED SINK, CONNECT TO EXISTING WASTE & H&CW SUPPLY, PROVIDE NEW H&CW STOP & P-TRAP.
 - (P3) 1/2" H&CW DOWN IN WALL, 1 1/2" VENT DOWN TO 3" WASTE BURIED 1 1/2" VENT UP IN WALL.
 - (P4) 1/2" H&CW DOWN IN WALL TO SHOWER VALVE.
 - (P5) 2" VENT UP IN WALL.
 - (P6) CONNECT NEW 1/2" H&CW, 2" VENT TO EXISTING H&CW & VENT ABOVE CEILING.
 - (P7) INSTALL NEW TOILET IN LOCATION OF REMOVED TOILET, CONNECT TO EXISTING SANITARY, PROVIDE NEW 1/2" CW SUPPLY & STOP.
 - (P8) CONNECT NEW 1/2" H&CW ABOVE CEILING.
 - (P9) CONNECT NEW 3" SAN TO EXISTING ABOVE CEILING.
 - (P10) 1/2" H&CW DOWN IN WALL, 2" WASTE DOWN TO FIRST FLOOR, 2" VENT UP IN WALL.
 - (P11) CONNECT NEW SINK TO EXISTING PLUMBING PIPING, PROVIDE NEW STOPS & P-TRAP.
 - (P12) 1/2" H&CW UP TO SECOND FLOOR, 1 1/2" WASTE DOWN FROM SECOND FLOOR.
 - (P13) 1/2" CW UP TO SECOND FLOOR, 1 1/2" WASTE DOWN FROM SECOND FLOOR.
 - (P14) NEW WALL HUNG AC UNIT, REFER TO MECHANICAL DRAWINGS, PROVIDE LINE SIZE CONDENSATE DRAIN TO PLUMBING WALL FOR INDIRECT CONNECTION, SEE DETAIL 5/P-201, PROVIDE ACCESS PANEL.
 - (P15) 1/2" CW, 2" VENT UP TO SECOND FLOOR.
 - (P16) 1/2" H&CW UP TO SECOND FLOOR, 2" WASTE DOWN FROM SECOND FLOOR.
 - (P17) 2" WASTE DOWN FROM SECOND FLOOR.
 - (P18) 2" VENT UP TO SECOND FLOOR.
 - (P19) 4" SAN DOWN IN PLUMBING WALL TO 4" SAN BURIED.
 - (P20) 4" SAN DOWN IN WALL TO 4" SAN BURIED.
 - (P21) NEW HEAT PUMP ABOVE CEILING, REFER TO MECHANICAL DRAWINGS, PROVIDE LINE SIZE COND DRAIN TO WASTE PIPE FOR INDIRECT CONNECTION.
 - (P22) INDIRECT CONNECTION, SEE DETAIL 5/P-201.
 - (P23) REINSTALL EXISTING CLINIC SINK, PROVIDE ALL NEW TRIM, SEE DETAIL 11/P-201.
 - (P24) INSTALL NEW SHOWER TRIM AND NEW DRAIN ON REWORKED SHOWER, CONNECT TO EXISTING WATER SUPPLIES.
 - (P25) FAUCET MOUNTED EMERGENCY EYEWASH, SEE DETAIL 12/P-201.
 - (P26) WALL MOUNTED EMERGENCY EYEWASH/DRENCH HOSE, SEE DETAIL 13/P-201, CONNECT NEW 1/2" H&CW TO EXISTING H&CW IN SPACE.
 - (P27) INSTALL NEW WATER COOLER IN LOCATION OF REMOVED, CONNECT TO EXISTING CW AND WASTE PIPING, PROVIDE NEW P-TRAP.
 - (P28) 2" VENT UP FROM FIRST FLOOR.
 - (P29) 1 1/2" WASTE DOWN TO FIRST FLOOR, 1 1/2" VENT UP IN WALL.
 - (P30) 3/4" CW, 1/2" HW UP FROM FIRST FLOOR, PIPE TO NEW TOILET AND LAV.
 - (P31) 1/2" H&CW UP FROM FIRST FLOOR TO SHOWER VALVE.
 - (P32) 1/2" H&CW UP FROM FIRST FLOOR, 1 1/2" WASTE DOWN TO FIRST FLOOR, 1 1/2" VENT UP IN WALL.
 - (P33) 1/2" CW UP FROM FIRST FLOOR.
 - (P34) 1/2" CW UP FROM FIRST FLOOR, 1 1/2" WASTE DOWN TO FIRST FLOOR, 1 1/2" VENT UP IN WALL.
 - (P35) NEW HEAT PUMP, REFER TO MECHANICAL DRAWINGS, CONNECT TO EXISTING CONDENSATE DRAIN, PROVIDE NEW P-TRAP.
 - (P36) NEW HEAT PUMP, REFER TO MECHANICAL DRAWINGS, PROVIDE NEW LINE SIZE CONDENSATE DRAIN TO EXISTING FLOOR DRAIN FOR INDIRECT CONNECTION.
 - (P37) 1/2" CW, 2" VENT UP FROM FIRST FLOOR.
 - (P38) (21) 1/2" H&CW DOWN IN WALL, 2" WASTE DOWN TO FIRST FLOOR, 2" VENT UP IN WALL.
 - (P39) (21) 1/2" CW DOWN IN WALL, 2" VENT UP FROM FIRST FLOOR, 3" VENT UP FROM FIRST FLOOR.
 - (P40) 1/2" CW DOWN IN WALL TO REFRIGERATOR, PROVIDE ISOLATION VALVE IN RECESSED CONNECTION BOX.
 - (P41) DISHWASHER, CONNECT TO PLUMBING AT ADJACENT SINK, SEE DETAIL 14/P-201.
 - (P42) 1/2" H&CW DOWN IN WALL, 2" WASTE DOWN TO 3" WASTE BURIED, 1 1/2" VENT UP IN WALL.

PLUMBING SECOND FLOOR CONSTRUCTION PLAN
SCALE: 1/8" = 1'-0"


REVISIONS NO.	DESCRIPTION	DATE
1	ADDENDUM 1	6/10/20

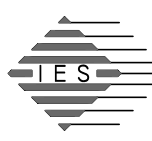


INNOVATIVE ENGINEERING SERVICES, LLC
AN INTEGRATED ENGINEERING & DESIGN FIRM
33 N PLAINFIELD INDUSTRIAL RD
WALLINGFORD, CT 06492
TEL: 203.667.1270
WWW.WEILLC.COM

KENT SUBSTANCE ABUSE CENTER
46 MAPLE STREET
KENT, CT 06757

**BIRCH HILL**
RECOVERY CENTER

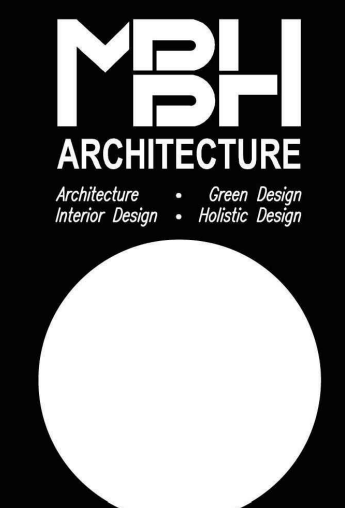
**MBH ARCHITECTURE**
Architecture • Green Design
Interior Design • Holistic Design

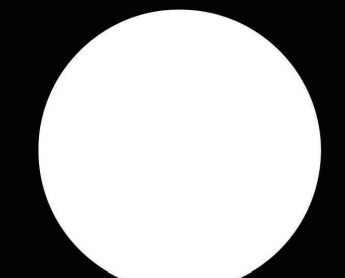


MBH ARCHITECTURE, LLC
Corporate Center West • 433 South Main Street
Suite 301 • West Hartford, Connecticut 06110
Tel: 860-521-1400 • Fax: 860-521-1400
www.mbharchitecture.com

ISSUED FOR:	100% CD's
DATE ISSUED:	3/6/2020
SCALE:	As indicated
PROJECT NUMBER:	17180
DRAWN BY:	JAG

P-120

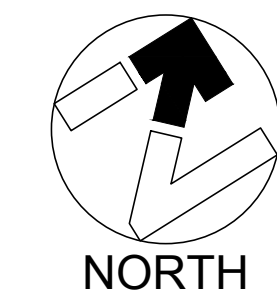

G:\ES Projects\2017 Projects\Team TEM\17093 Apple Rehab Kent CT\Contract Documents\17093_P-121.dwg Plotted by cmassaro on Sep 10, 2020 - 4:03pm

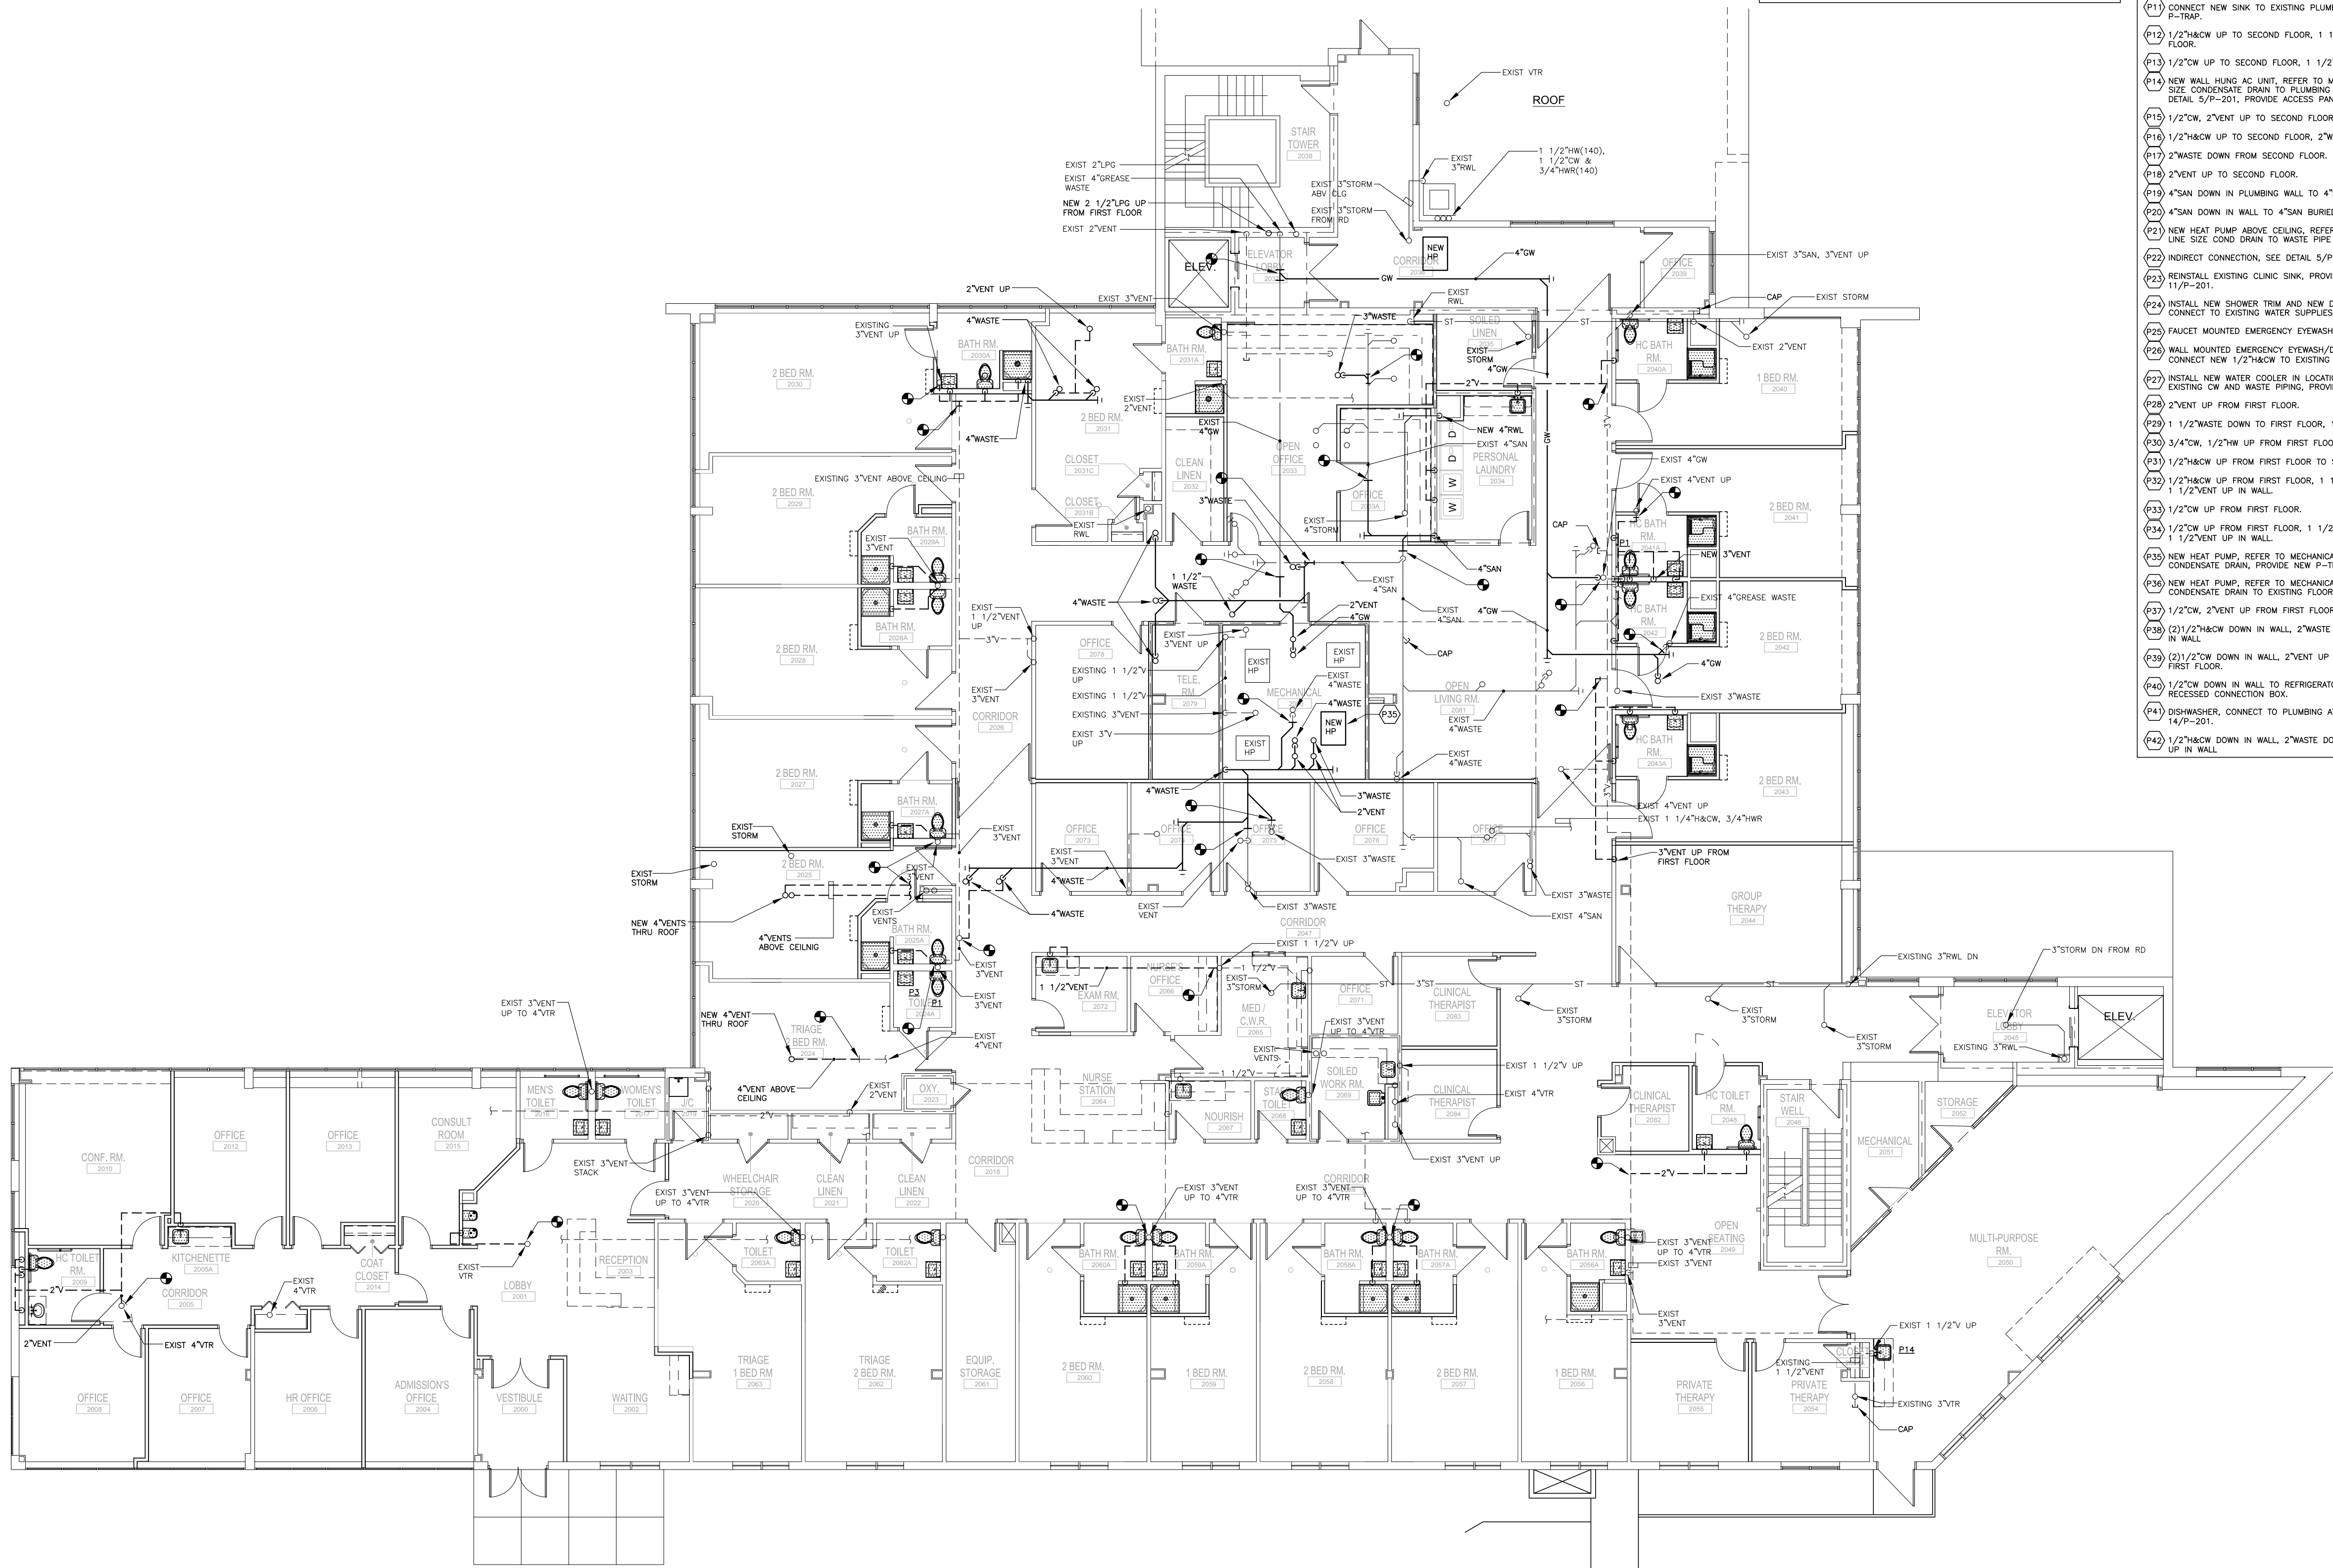

PLUMBING SECOND FLOOR CONSTRUCTION PLAN ABOVE CEILING WASTE AND VENT PIPING
SCALE: 1/8" = 1'-0"

ISOLATION VALVE ACCESS NOTE

ALL ISOLATION VALVES SHALL BE LOCATED ABOVE AN ACCESSIBLE CEILING, NO ISOLATION VALVES SHALL BE INSTALLED IN PATIENT ROOMS OR PATIENT BATHROOMS REGARDLESS OF THE CEILING PROVIDED.

NEW CONCEALED PLUMBING PIPING

CONTRACTOR SHALL BE RESPONSIBLE FOR CUTTING OPEN EXISTING WALLS AS REQUIRED FOR THE INSTALLATION OF NEW PLUMBING PIPING. CONTRACTOR SHALL ALSO BE RESPONSIBLE FOR PATCHING EXISTING WALLS, PATCH SHALL MATCH EXISTING.

GREASE WASTE PIPING

ALL EXISTING GREASE WASTE PIPE TO BE REUSED SHALL BE CLEANED AND POWER FLUSHED TO FULL CAPACITY.

PLUMBING KEY NOTES

- (P1) INSTALL NEW TOILET IN LOCATION OF THE REMOVED TOILET, CONNECT TO EXISTING SANITARY & CW SUPPLY, PROVIDE NEW CW STOP.
- (P2) INSTALL NEW SINK IN LOCATION OF REMOVED SINK, CONNECT TO EXISTING WASTE & H&CW SUPPLY, PROVIDE NEW H&CW STOP & P-TRAP.
- (P3) 1/2" H&CW DOWN IN WALL, 1 1/2" WASTE DOWN TO 3" WASTE BURIED 1 1/2" VENT UP IN WALL.
- (P4) 1/2" H&CW DOWN IN WALL TO SHOWER VALVE.
- (P5) 2" VENT UP IN WALL.
- (P6) CONNECT NEW 1/2" H&CW, 2" VENT TO EXISTING H&CW & VENT ABOVE CEILING.
- (P7) INSTALL NEW TOILET IN LOCATION OF REMOVED TOILET, CONNECT TO EXISTING SANITARY, PROVIDE NEW 1/2" CW SUPPLY & STOP.
- (P8) CONNECT NEW 1/2" H&CW ABOVE CEILING.
- (P9) CONNECT NEW 3" SAN TO EXISTING ABOVE CEILING.
- (P10) 1/2" H&CW DOWN IN WALL, 2" WASTE DOWN TO FIRST FLOOR, 2" VENT UP IN WALL.
- (P11) CONNECT NEW SINK TO EXISTING PLUMBING PIPING, PROVIDE NEW STOPS & P-TRAP.
- (P12) 1/2" H&CW UP TO SECOND FLOOR, 1 1/2" WASTE DOWN FROM SECOND FLOOR.
- (P13) 1/2" CW UP TO SECOND FLOOR, 1 1/2" WASTE DOWN FROM SECOND FLOOR.
- (P14) NEW WALL HUNG AC UNIT, REFER TO MECHANICAL DRAWINGS, PROVIDE LINE SIZE CONDENSATE DRAIN TO PLUMBING WALL FOR INDIRECT CONNECTION, SEE DETAIL 5/P-201, PROVIDE ACCESS PANEL.
- (P15) 1/2" CW, 2" VENT UP TO SECOND FLOOR.
- (P16) 1/2" H&CW UP TO SECOND FLOOR, 2" WASTE DOWN FROM SECOND FLOOR.
- (P17) 2" WASTE DOWN FROM SECOND FLOOR.
- (P18) 2" VENT UP TO SECOND FLOOR.
- (P19) 4" SAN DOWN IN PLUMBING WALL TO 4" SAN BURIED.
- (P20) 4" SAN DOWN IN WALL TO 4" SAN BURIED.
- (P21) NEW HEAT PUMP ABOVE CEILING, REFER TO MECHANICAL DRAWINGS, PROVIDE LINE SIZE COND DRAIN TO WASTE PIPE FOR INDIRECT CONNECTION.
- (P22) INDIRECT CONNECTION, SEE DETAIL 5/P-201.
- (P23) REINSTALL EXISTING CLINIC SINK, PROVIDE ALL NEW TRIM, SEE DETAIL 11/P-201.
- (P24) INSTALL NEW SHOWER TRIM AND NEW DRAIN ON REWORKED SHOWER, CONNECT TO EXISTING WATER SUPPLIES.
- (P25) FAUCET MOUNTED EMERGENCY EYEWASH, SEE DETAIL 12/P-201.
- (P26) WALL MOUNTED EMERGENCY EYEWASH/DRENCH HOSE, SEE DETAIL 13/P-201, CONNECT NEW 1/2" H&CW TO EXISTING H&CW IN SPACE.
- (P27) INSTALL NEW WATER COOLER IN LOCATION OF REMOVED, CONNECT TO EXISTING CW AND WASTE PIPING, PROVIDE NEW P-TRAP.
- (P28) 2" VENT UP FROM FIRST FLOOR.
- (P29) 1 1/2" WASTE DOWN TO FIRST FLOOR, 1 1/2" VENT UP IN WALL.
- (P30) 3/4" CW, 1/2" HW UP FROM FIRST FLOOR, PIPE TO NEW TOILET AND LAV.
- (P31) 1/2" H&CW UP FROM FIRST FLOOR TO SHOWER VALVE.
- (P32) 1/2" H&CW UP FROM FIRST FLOOR, 1 1/2" WASTE DOWN TO FIRST FLOOR, 1 1/2" VENT UP IN WALL.
- (P33) 1/2" CW UP FROM FIRST FLOOR.
- (P34) 1/2" CW UP FROM FIRST FLOOR, 1 1/2" WASTE DOWN TO FIRST FLOOR, 1 1/2" VENT UP IN WALL.
- (P35) NEW HEAT PUMP, REFER TO MECHANICAL DRAWINGS, CONNECT TO EXISTING CONDENSATE DRAIN, PROVIDE NEW P-TRAP.
- (P36) NEW HEAT PUMP, REFER TO MECHANICAL DRAWINGS, PROVIDE NEW LINE SIZE CONDENSATE DRAIN TO EXISTING FLOOR DRAIN FOR INDIRECT CONNECTION.
- (P37) 1/2" CW, 2" VENT UP FROM FIRST FLOOR.
- (P38) (Q21) 2" H&CW DOWN IN WALL, 2" WASTE DOWN TO FIRST FLOOR, 2" VENT UP IN WALL.
- (P39) (Q21) 2" CW DOWN IN WALL, 2" VENT UP FROM FIRST FLOOR, 3" VENT UP FROM FIRST FLOOR.
- (P40) 1/2" CW DOWN IN WALL TO REFRIGERATOR, PROVIDE ISOLATION VALVE IN RECESSED CONNECTION BOX.
- (P41) DISHWASHER, CONNECT TO PLUMBING AT ADJACENT SINK, SEE DETAIL 14/P-201.
- (P42) 1/2" H&CW DOWN IN WALL, 2" WASTE DOWN TO 3" WASTE BURIED, 1 1/2" VENT UP IN WALL.

KENT SUBSTANCE ABUSE CENTER

46 MAPLE STREET
KENT, CT 06757



MBH
ARCHITECTURE
Architecture • Green Design
Interior Design • Holistic Design

MBH ARCHITECTURE, LLC
Corporate Center West • 423 South Main Street
Suite 201 • West Hartford, Connecticut 06110
Tel: 860-521-1400 • Fax: 860-521-9400
www.mbharchitecture.com

ISSUED FOR: 100% CD's
DATE ISSUED: 3/6/2020
SCALE: As indicated
PROJECT NUMBER: 17180
DRAWN BY: JAG

P-121

